



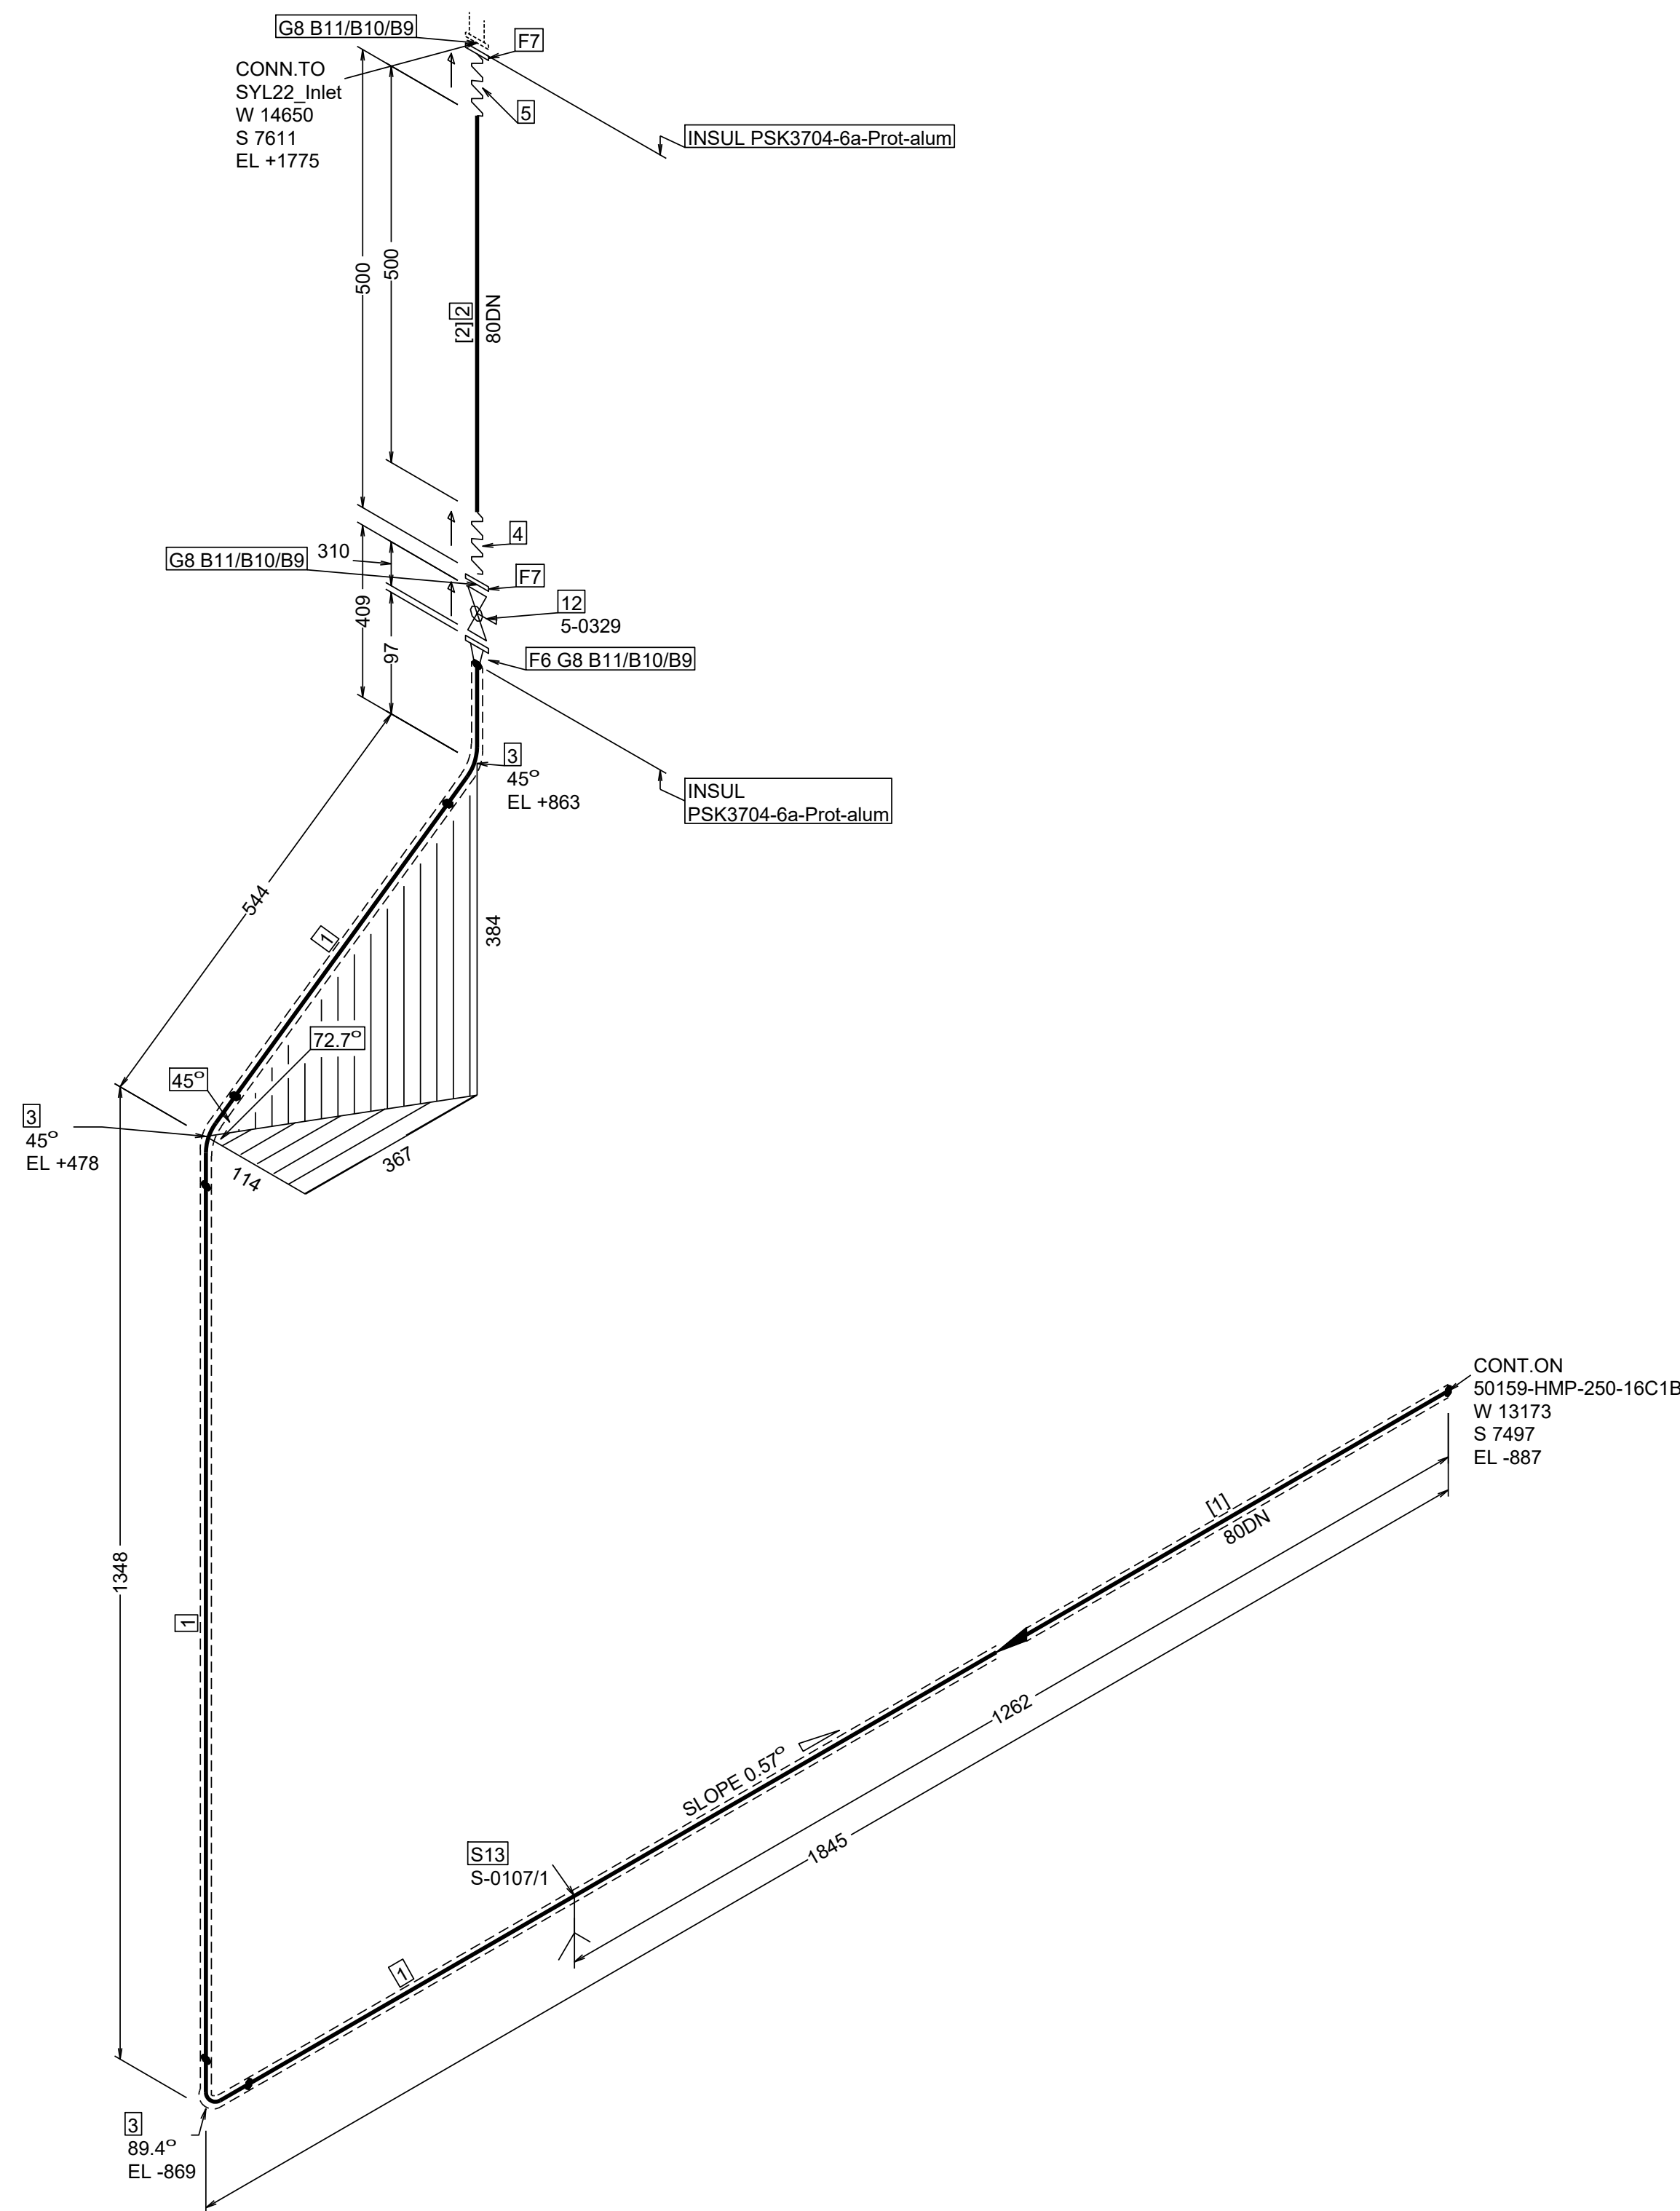

NO	PART DESCRIPTION	DN (MM)	PIPE SPEC	QUANTITY
1	Tube - 88.9 x 3.20 - EN 10216-2 - P235GH-TC1	80	119440-VE16C1C-R00	3369MM
2	HOSE	80	HOSES	500MM
3	Elbow - EN 10253-2 - type A - model 3D - 90deg - 88.9 x 3.20 - P235GH-TC1	80	119440-VE16C1C-R00	3
4	HOSE PROVIDED BY KADANT	80	HOSES	1
5	HOSE	80	HOSES	1
6	Weld-neck flange - EN 1092-1 - type 11 - B1 - 88.9/DN80 - PN16 - P250GH	80	119440-VE16C1C-R00	1
7	Dummy wn flange - DIN 2633 80x88.9 PN16 Delivered with component	80	DUMMY-FLANGES	2
NO	PART DESCRIPTION	DN (MM)	PIPE SPEC	QUANTITY
8	Gasket - EN 1514-1 - type IBC - OD88.9/DN80 - 1.5mm Thk - PN40 Fiber	80	119440-VE16C1C-R00	3
9	70 mm Bolt EN ISO 4014 25CrMo4, EN 10269, mat cert. 3.1, HDG	16		24
10	Hexagon nut EN ISO 4032 25CrMo4, EN 10269, mat cert. 3.1, HDG	16		24
11	Washer EN ISO 7089 Grade A - S235JR EN10025-2 - HDG	16		48
12	CPK BASIC BALL VALVE FLANGED PN16 RF WI HAND LEVER 5-0329	80	KBE/VALV01	1
	<u>SUPPORTS</u>			
13	HANGER PSK 7303 TYPE 12 See supportlist	80	VOFSUPP-PRIM-PSK-AT TA	1

PIPE SPOOLS

[1] [2]

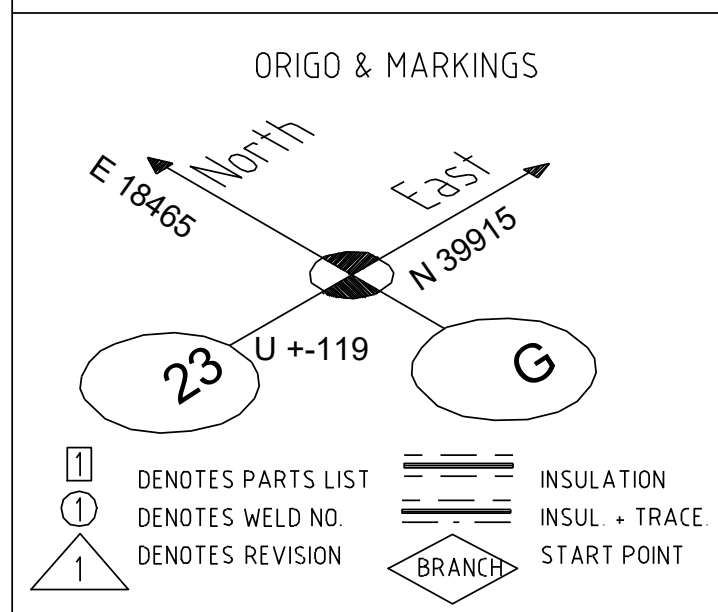

Insulation table (lengths according SSG 7645 Alt2)			
Bore	Thickness	Length	Insulation spec name
80	40mm	3914mm	/PSK3704-6a-Prot-alum

NOTE:

Site weldings to be added by contractor.

Buildings construction and equipment erection tolerances to be checked by contractor.

Pipe levels and dimensions are according to pipe center line.

Isometric drawings for sizes DN 15-25 are approximate.
Piping contractor is responsible for final routing and supporting.

Welding factor	Acc. to pipe class
Efficiency of long weld	Acc. to pipe class
NDT circ. weld %	-
NDT long weld %	-
Welding list see doc.	-

		Hazardous CLP content		Degree of prohibition to be decided by contractor.	
Rev	Revision Note			Created by	Checked by
0				J. Lakka	T. Saarinen
Design press. (min)	-1bar	Pipe Class	/119440-VE16C1C-R00	M. Kankkunen	
Design temp. (min)	-	PED Category	I	5/5/2026	
Max. allow. press. (PS)	-	Media		Site	Equipment Type
Operating press.	5.9bar	P&ID	RAU8F00303	Tervasaari, Valkeakoski	Höyry- ja lauhdejärjestelmä
Operating temp.	181degC	Design press.	6bar	Project Key	Project Name
PED Module	-	Design temp.	220degC	TERPM5, IN265A	Tor PM 5-Safe Future
PED Group	-	Test press.	-	Project Number	Work
Wind loads	-	Pipe list doc. ID	RAUAF04300	NS265A	
External loads	-	Valve list doc. ID	RAUAF04301	Scale	Size
				Weight	
				 This document is the exclusive intellectual property of Valmet Corporation and/or its subsidiaries (collectively and individually "Valmet") and is furnished solely for executing and maintaining the specific project. Re-use of the document for any other project or purpose is prohibited. The document or the information shall not be reproduced, copied or disclosed to any third party without the prior written consent of Valmet. By accessing this document, you accept these terms of use.	
				Title	
				50183-HMP-80-16C1B	
				Status	Document ID
				CERTIFIED	
				Security Classification	Sheet
				Internal	1 / 1
					Revision
					0