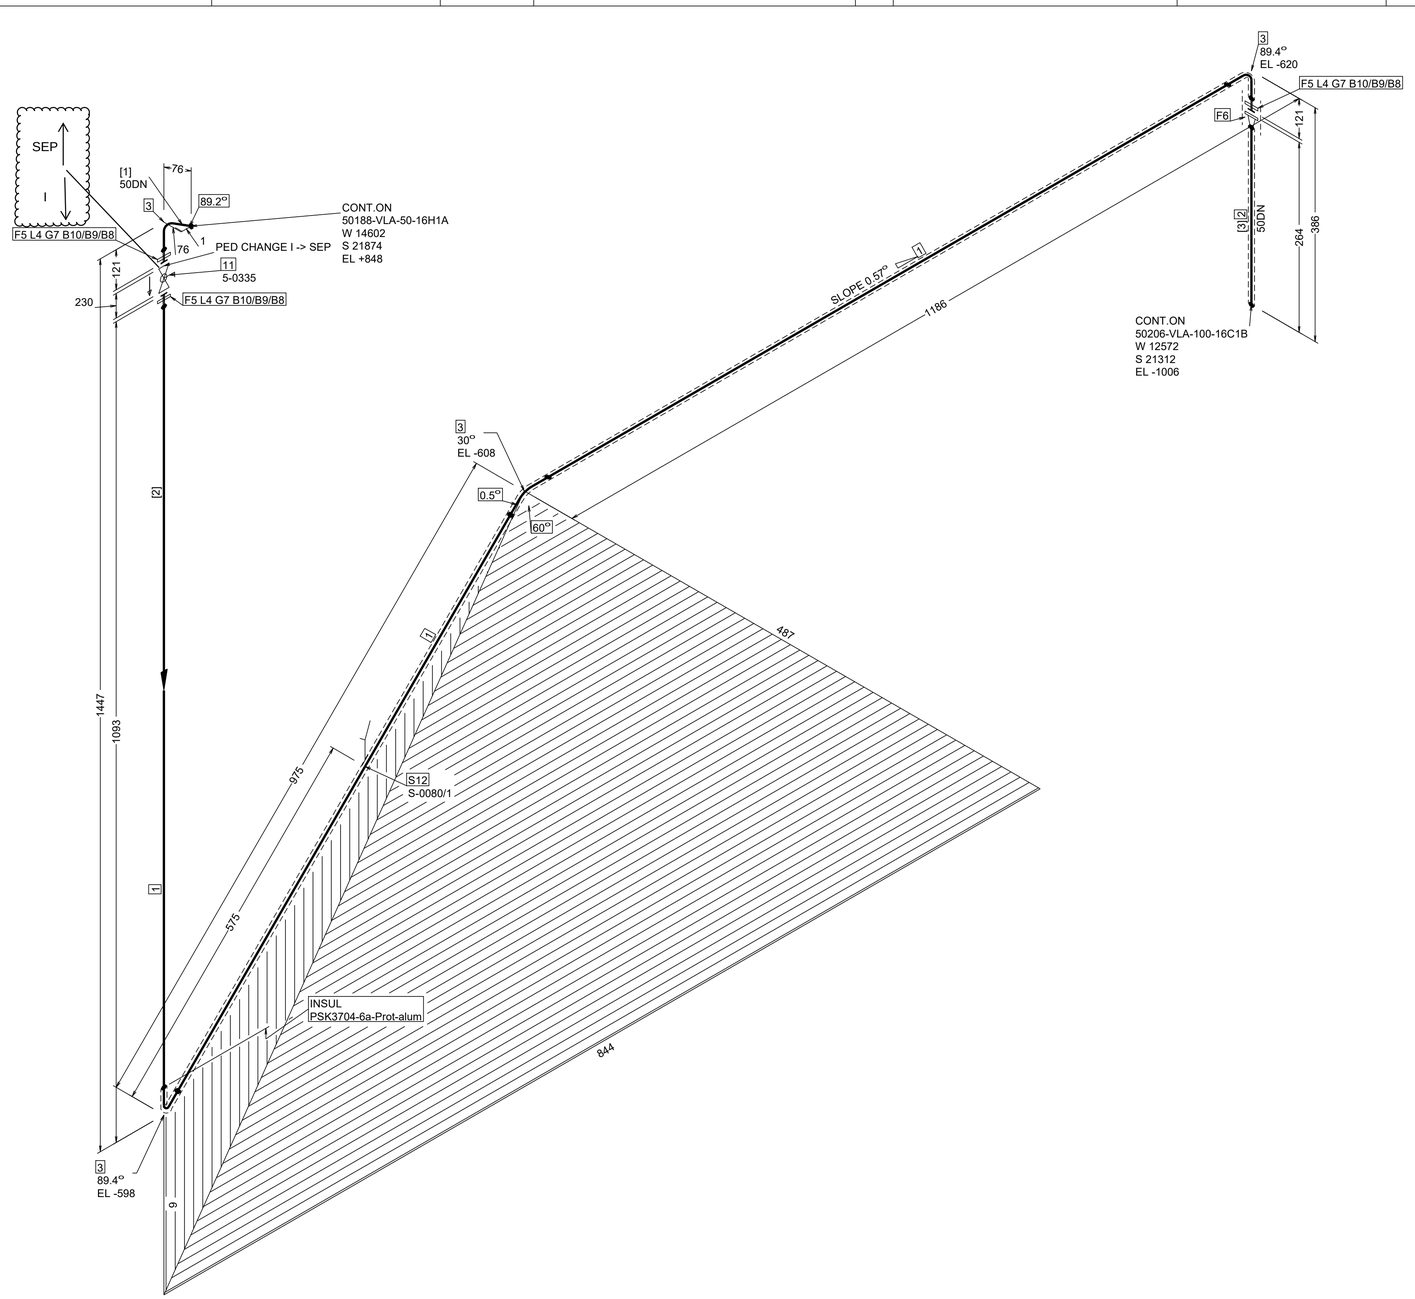


NO	PART DESCRIPTION	DN (MM)	PIPE SPEC	QUANTITY
1	Tube - 60.3 x 2.00 - EN 10217-7 - 1.4307-TC1	50	119440-VE16H1A-R00	2942MM
2	Tube - 60.3 x 2.90 - EN 10216-2 - P235GH-TC1	50	119440-VE16C1C-R00	216MM
3	Elbow - w - EN 10253-4 - type A - Table A.1 - model 3D - 90deg - 60.3 x 2.00 - 1.4307	50	119440-VE16H1A-R00	4
4	Weldring neck - EN 1092-1 - type 35 - 60.3/DN50 - PN16 - 1.4307	50	119440-VE16H1A-R00	3
5	Loose flange - EN 1092-1 - type 02 - - 60.3/DN50 - PN40 - P265GH HDG	50	119440-VE16H1A-R00	3
6	Weld-neck flange - EN 1092-1 - type 11 - B1 - 60.3/DN50 - PN40 - P250GH	50	119440-VE16C1C-R00	1

NO	PART DESCRIPTION	DN (MM)	PIPE SPEC	QUANTITY
7	Gasket - EN 1514-1 - type IBC - OD60.3/DN50 - 1.5mm Thk - PN40 Fiber	50	119440-VE16H1A-R00	3
8	80 mm Bolt EN ISO 4014 25CrMo4, EN 10269, mat cert. 3.1, HDG	16		12
9	Hexagon nut EN ISO 4032 25CrMo4, EN 10269, mat cert. 3.1, HDG	16		12
10	Washer EN ISO 7089 Grade A - S235JR EN10025-2 - HDG	16		24
11	KPK BASIC BALL VALVE FLANGED PN16 RF WI HAND LEVER 5-0335	50	KBE/VALV01	1
	SUPPORTS			
12	SLIDE SUPPORT PSK 7303 TYPE 1, LOW See supportlist	50	VOFSUPP-PRIM-PSK-ATTA	1

PIPE SPOOLS

[1] [2] [3]

ORIGO & MARKINGS

North E 18465 East N 39915 23 U +-119 G

1 DENOTES PARTS LIST
1 DENOTES WELD NO.
1 DENOTES REVISION
INSULATION
INSUL. + TRACE
BRANCH START POINT

Insulation table (lengths according SSG 7645 Alt2)			
Bore	Thickness	Length	Insulation spec name
50	40mm	2671mm	/PSK3704-6a-Prot-alum

NOTE:

Site weldings to be added by contractor.

Buildings construction and equipment erection tolerances to be checked by contractor.

Pipe levels and dimensions are according to pipe center line.

Isometric drawings for sizes DN 15-25 are approximate.
Piping contractor is responsible for final routing and supporting.

			Hazardous CLP content		
Directive	2014/68/EU	Pipe Class	/119440-VE16H1A-R00		
Design press. (min)	-1bar	PED Category	I / SEP		
Design temp. (min)	-	Media			
Max. allow. press. (PS)	-	Standard			
Operating press.	5.7bar	P&ID	RAU8F00303		
Welding factor	Acc. to pipe class	Operating temp.	164degC	Design press.	6bar
Effiency of long. weld	Acc. to pipe class	PED Module	-	Design temp.	220degC
NDT circ. weld %	-	PED Group	-	Test press.	-
NDT long. weld %	-	Wind loads	-	Pipe list doc. ID	RAUAF04300
Welding list see doc.	-	External loads	-	Valve list doc. ID	RAUAF04301

For installation tolerances dimensions to be checked by pipe contractor at site.
Degree of prefabrication to be decided by contractor.

Rev	Revision Note	Created by	Checked by	Approved by	Date
1	PED change location added	J. Lakka	T. Saarinen	M. Kankkunen	28/5/2026
0		J. Lakka	T. Saarinen	M. Kankkunen	5/5/2026

Site: Tervasaari, Valkeakoski
Equipment Type: Höyry- ja lauhdejärjestelmä
Equipment ID:
Project Key: TERPM5_N5265A
Project Name: Ter PM 5 Safe Future
Project Number: N5265A
Work:
Projection Method:
Welding Symbols: ISO 2553
General Tolerances: ISO 13 920-BF ISO 2768-mK-E ISO 2768-mK-E ISO 2768-mK-E
Scale: -
Size: A1
Weight: -

This document is the exclusive intellectual property of Valmet Corporation and/or its subsidiaries (collectively and individually "Valmet") and is furnished solely for executing and maintaining the specific project. Re-use of the document for any other project or purpose is prohibited. The document or the information shall not be reproduced, copied or disclosed to any third party without the prior written consent of Valmet. By accessing this document, you accept these terms of use.

Title: 50189-VLA-50-16H1A

Status: CERTIFIED
Document ID:
Sheet: 1/ 1
Security Classification: Internal
Revision: 1

Project: VKB Zone: PD1-BMA/DESI/PIPE/VLA MDB: /119440.005 DB: PREPAA/PREPAA Session: 4710 29/05/2026